



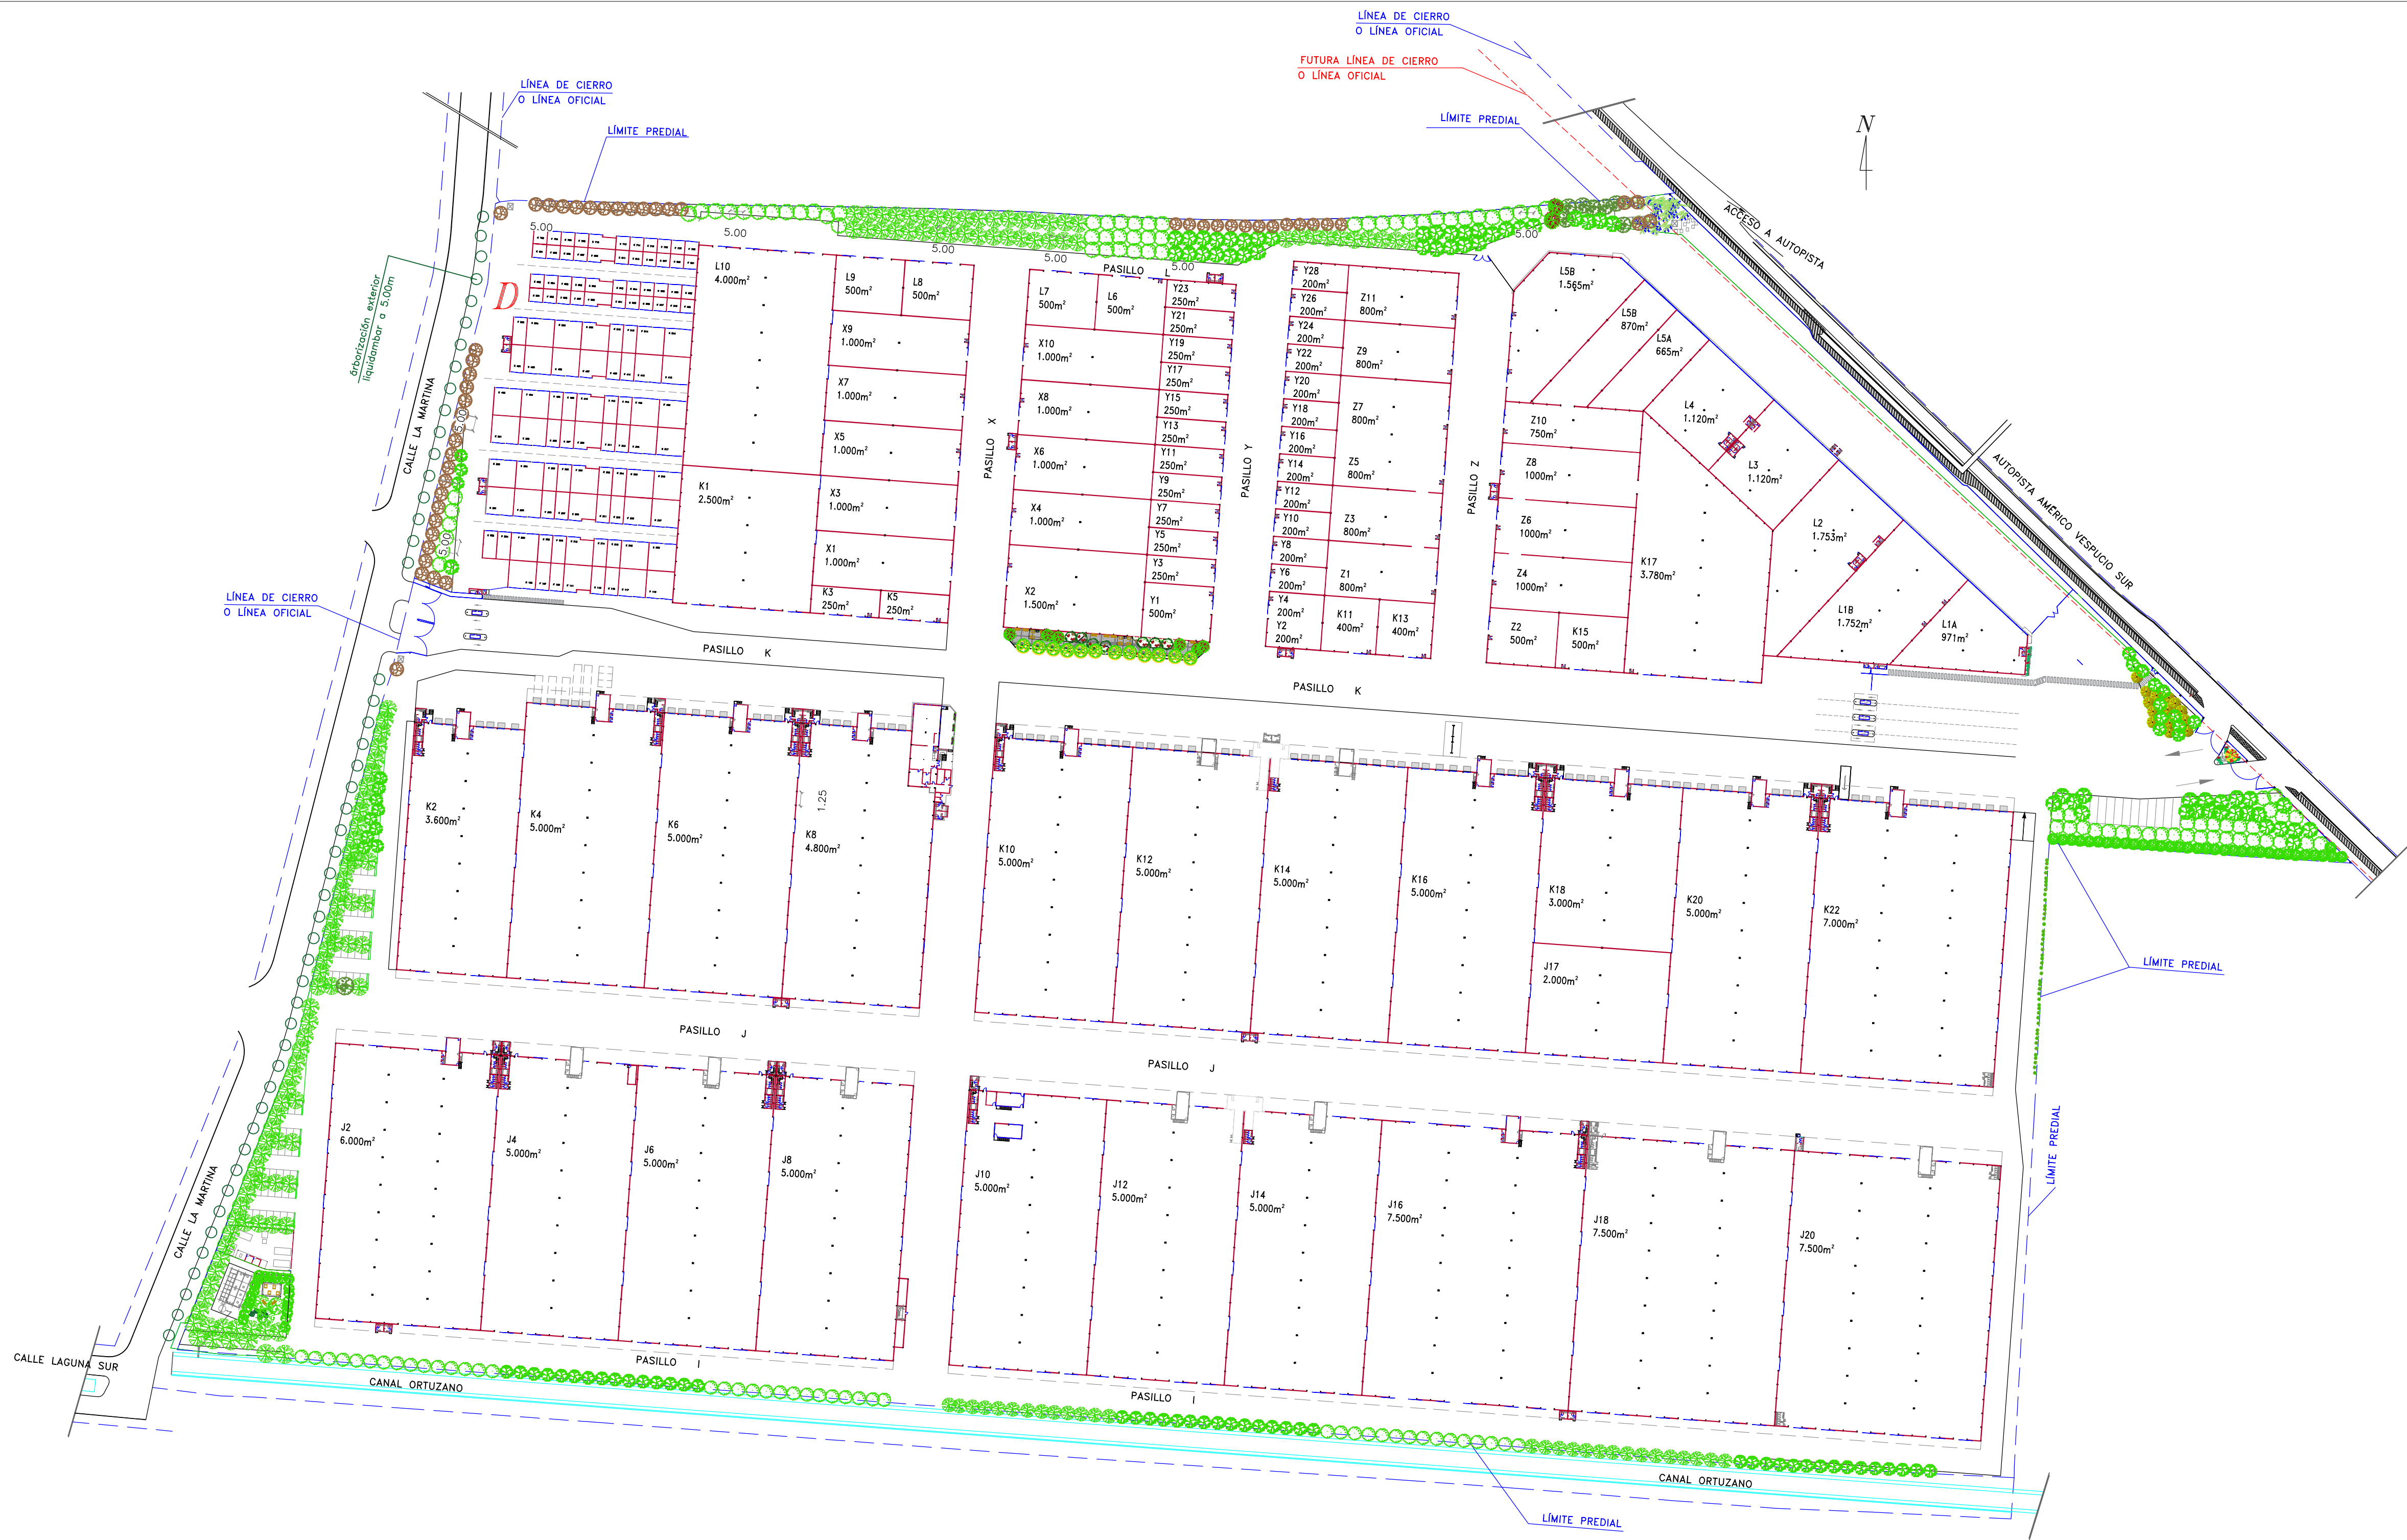


Porcentaje de nativas e introducidas "por especie"

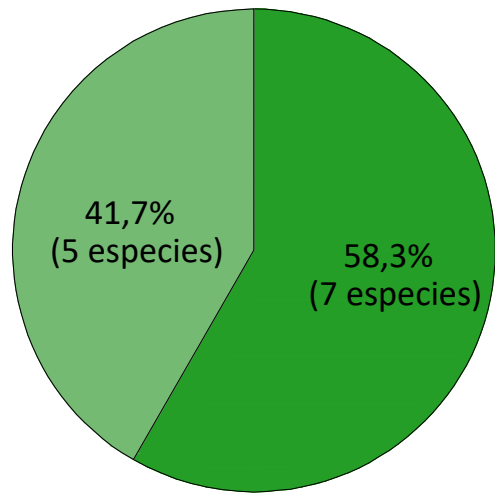

Nativas Introducidas

Porcentaje de "individuos" nativos e introducidos

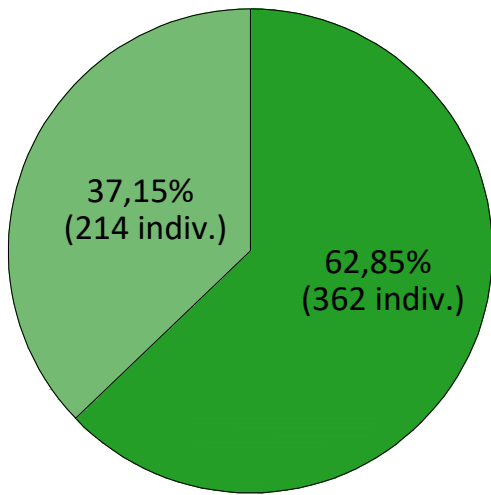


Nativas Introducidas

Áreas Verdes	
Árboles	
Árborización total: 13.041m2	
Nativos	Introducidos
4.00 Tora Cassipouira spinoza	4.00 Mioporum Mioporum
5.00 Huigón Schinus molle	5.00 Parkinsonia Parkinsonia
6.00 Molén Myrsine laevis Opuntia sp.	6.00 Ligustro Ligustro Ligustro
7.00 Algarrobo Chileno Prosopis chilensis	7.00 Liquidambar Liquidambar styraciflua
9.00 Quillay Quillay salicaria	9.00 Tulipero Tulipero
10.00 Pimiento Schinus molle	
Especies nativas e introducidas, referencia de algunas	
www.mma.cl/areas-verdes-inteligentes	
Árborización: -Existente: 51%, 4013m2 individuos entre 3.00m y 7.00m de altura. -Futura plant. 49%, 9.028m2 especies entre 1.00m a 2.20m de altura.	
Arbustos-Enredaderas- -Gramíneas	
-Abeila -Ampelopsis -Borró -Cotoneaster -Laurel de flor -Lavanda inglesa -Nandina -Penstemon -Plumbago -Rhus -Verónica	Abeila grandiflora Parthenocissus quinquefolia Arundinaria japonica Cotoneaster horizontalis Nerium oleander Lavandula officinalis Nandina domestica Penstemon rugellianus Plumbago Rhus ornata Veronica spicata

NOTAS:

LEYENDA:

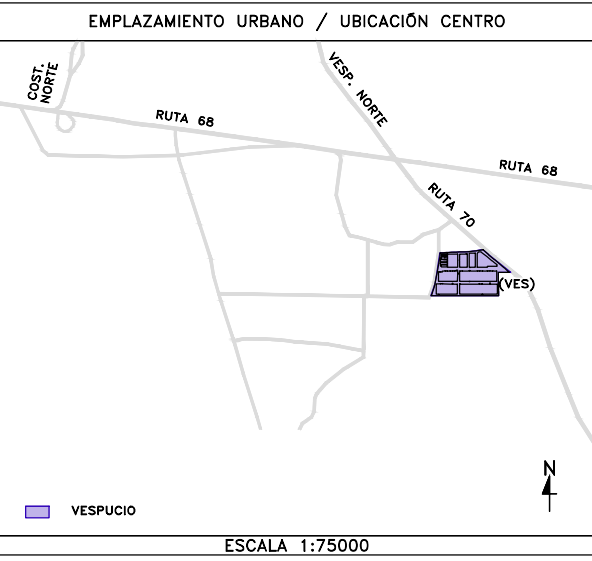

Inversiones Quildos Limitada

PROYECTO:

ÁREAS VERDES.

CONTENIDO:

PLANTA GENERAL Y ARBORIZACIÓN.

UBICACIÓN:

CENTRO VESPUCIO

PROPIETARIO:

BODEGAS SAN FRANCISCO

ARQUITECTO:

LUIZ ARRABO

CALCULISTA:

PROYECTISTA:

ROL:

Nº:

ESCALA:

FECHA:

REVISIONES			
REV. Nº	OBSERVACIONES	FECHA	APRUEBA
-	-	-	-
-	-	-	-
-	-	-	-
-	-	-	-
-	-	-	-
-	-	-	-

FIRMAS	
REVISIÓN:	VERIFICACIÓN:
VALIDACIÓN:	CLIENTE: