


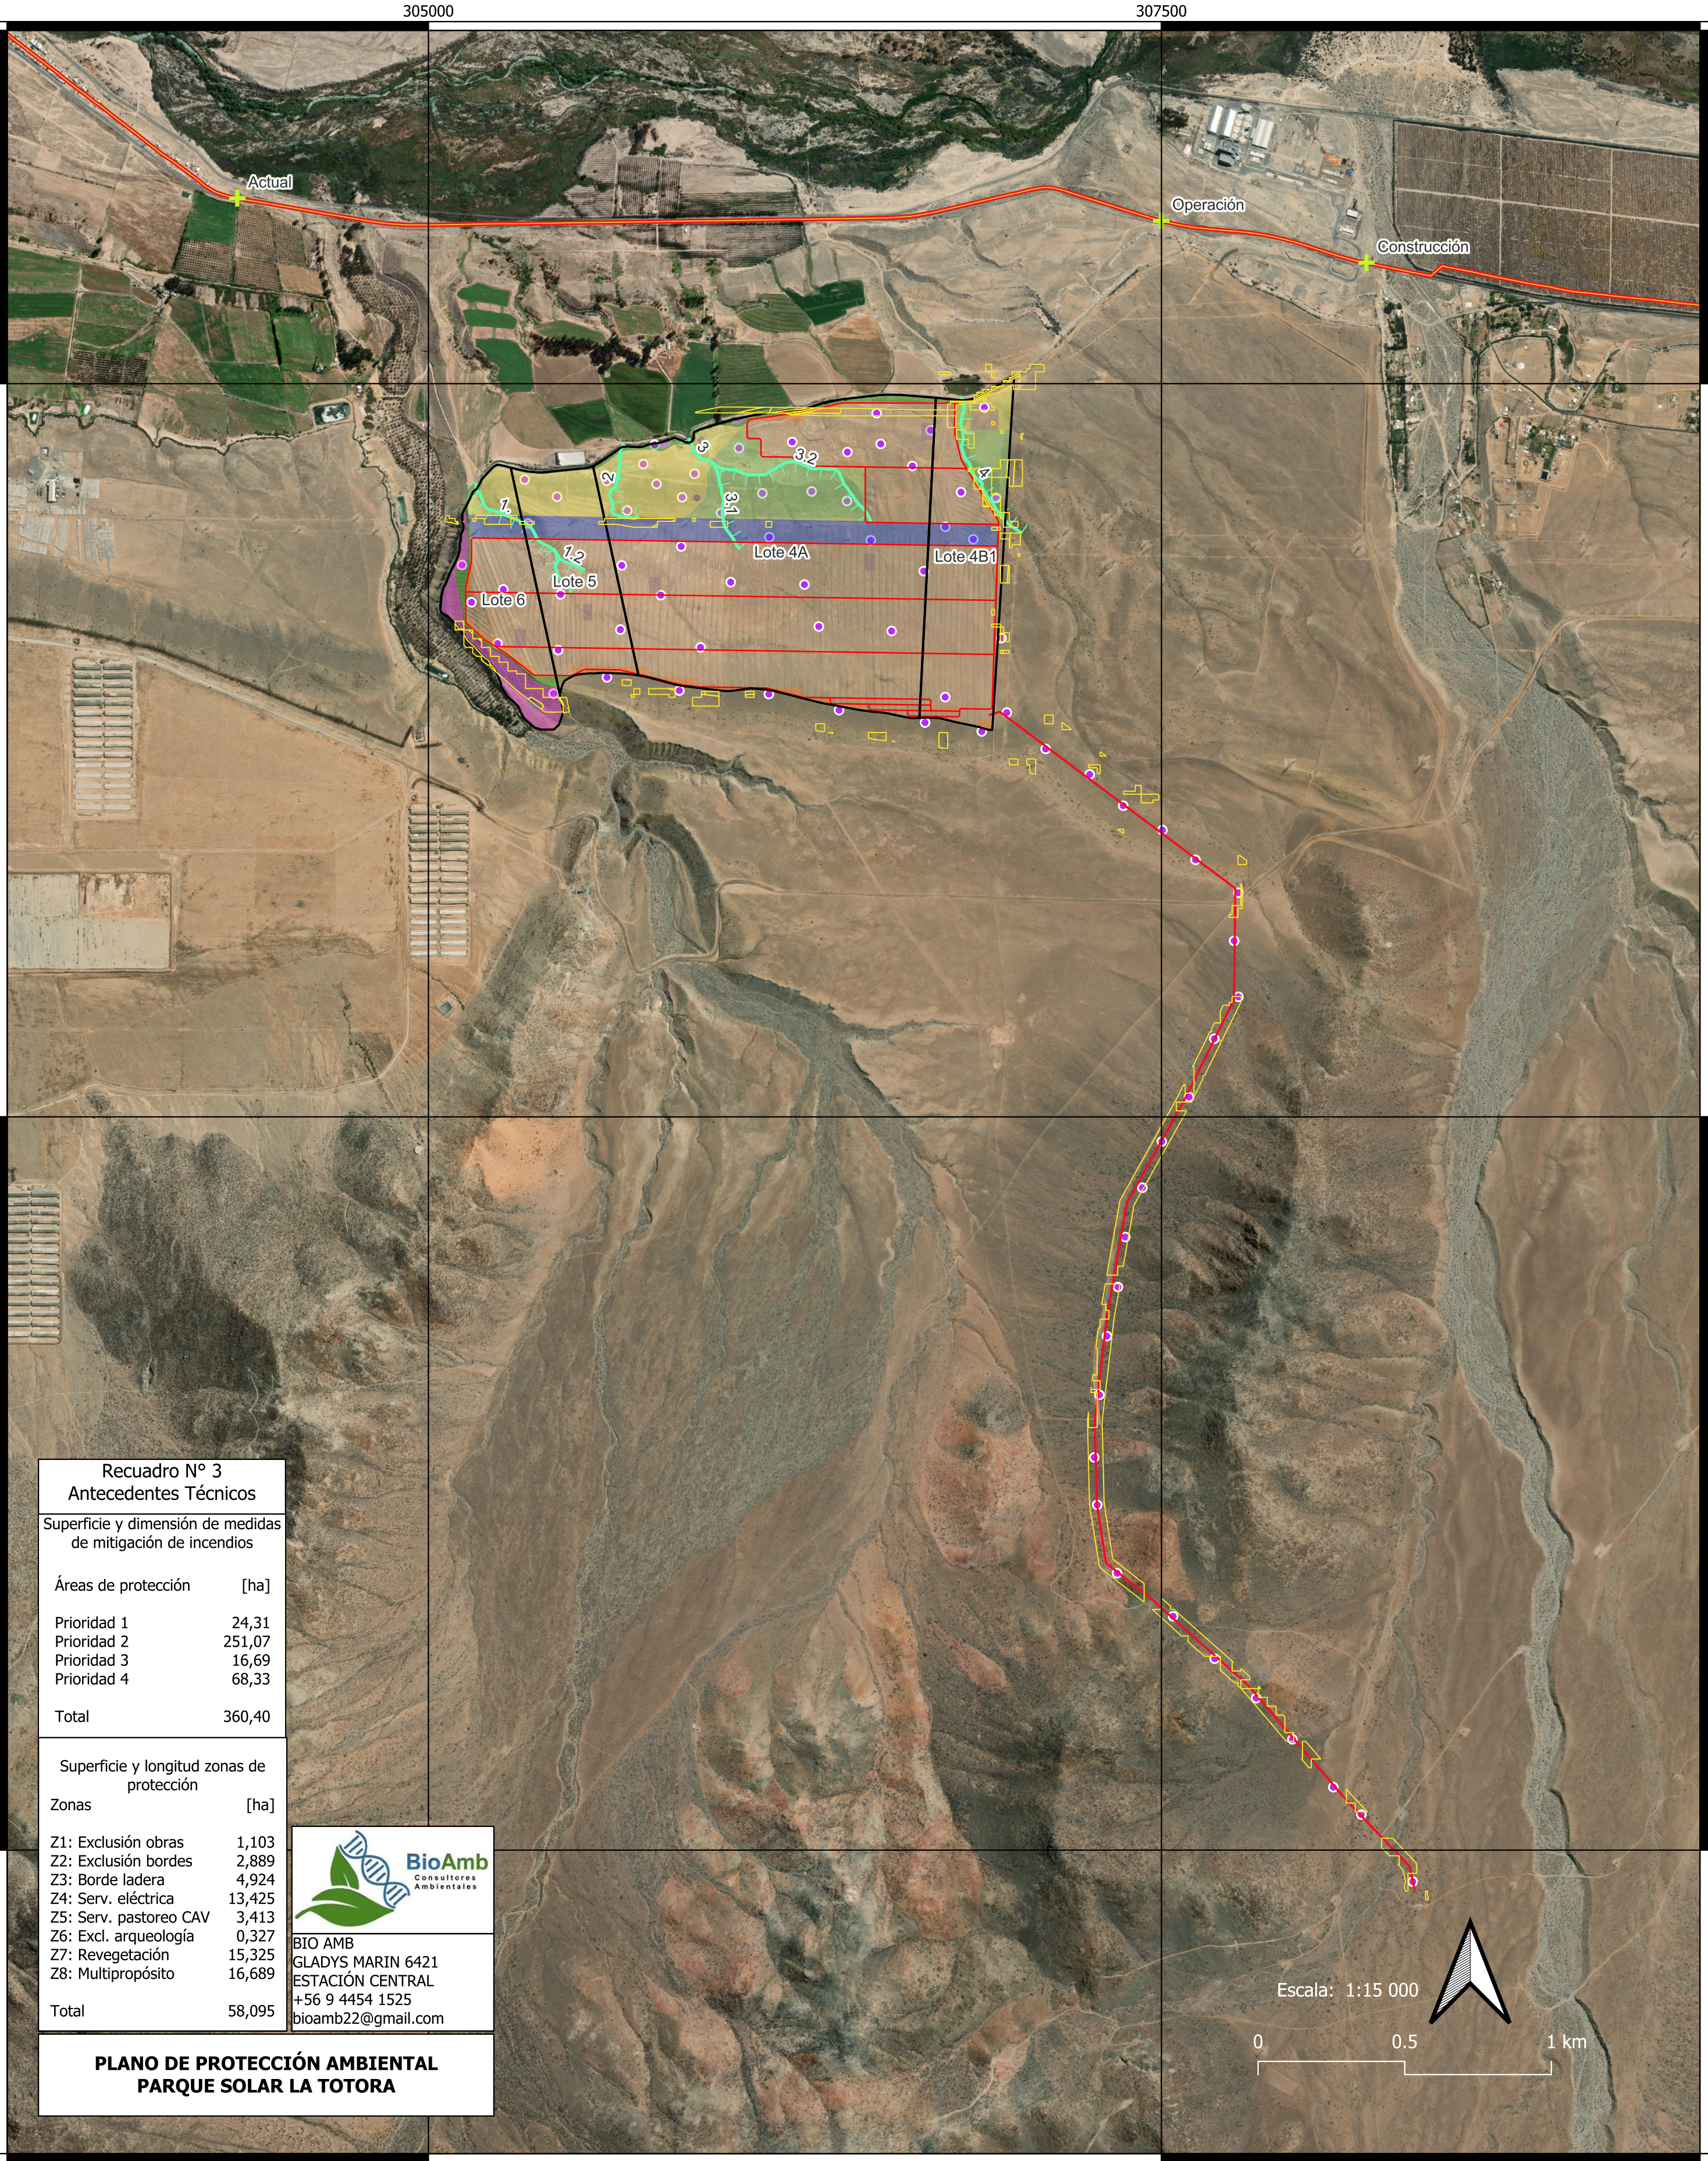

Recuadro N° 3
Antecedentes Técnicos

Superficie y dimensión de medidas de mitigación de incendios

Áreas de protección	[ha]
Prioridad 1	24,31
Prioridad 2	251,07
Prioridad 3	16,69
Prioridad 4	68,33
Total	360,40


Superficie y longitud zonas de protección

Zonas	[ha]
Z1: Exclusión obras	1,103
Z2: Exclusión bordes	2,889
Z3: Borde ladera	4,924
Z4: Serv. eléctrica	13,425
Z5: Serv. pastoreo CAV	3,413
Z6: Excl. arqueología	0,327
Z7: Revegetación	15,325
Z8: Multipropósito	16,689
Total	58,095



BIO AMB
GLADYS MARIN 6421
ESTACIÓN CENTRAL
+56 9 4454 1525
bioamb22@gmail.com

PLANO DE PROTECCIÓN AMBIENTAL
PARQUE SOLAR LA TOTORA

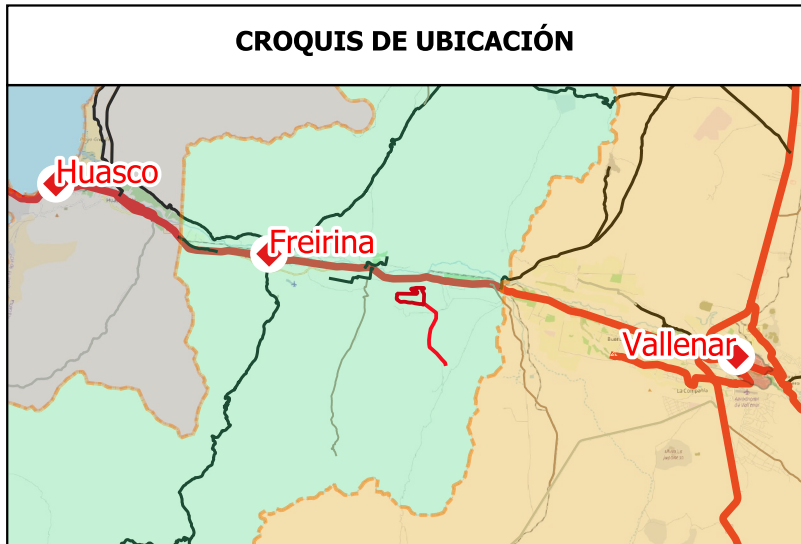

Recuadro N° 1
Antecedentes Prediales

Predio: La Totorá
Rol de Avalúo: 106-34, 106-33, 106-36, 106-38
Región: Atacama
Provincia: Huasco
Comuna: Freirina
Superficie: 169,8 ha

Recuadro N° 2
Antecedentes Cartográficos

Base Cartográfica:
DATUM WGS84, Huso 19
Escala 1:15.15000

Recuadro N° 4
Simbología

La Totorá - Freirina	Zonas Protección
Accesos	Z1
Lote	Z2
Trazado LAT	Z3
Caminos Internos	Z4
"Quebradas"	Z5
Parcelas	Z6
Prioridad 1	Z7
Ruta C-46	Z8

Recuadro N° 5
Antecedentes Administrativos

Interesado: Parsossy Sunna SpA

Autor: Jaime Vargas C.
Fecha: Ago. 29, 2024

Recuadro N° 6
Uso CONAF

Número de Solicitud

Fecha de Ingreso

Firma Analista

Timbre CONAF

Aprobado/Denegado