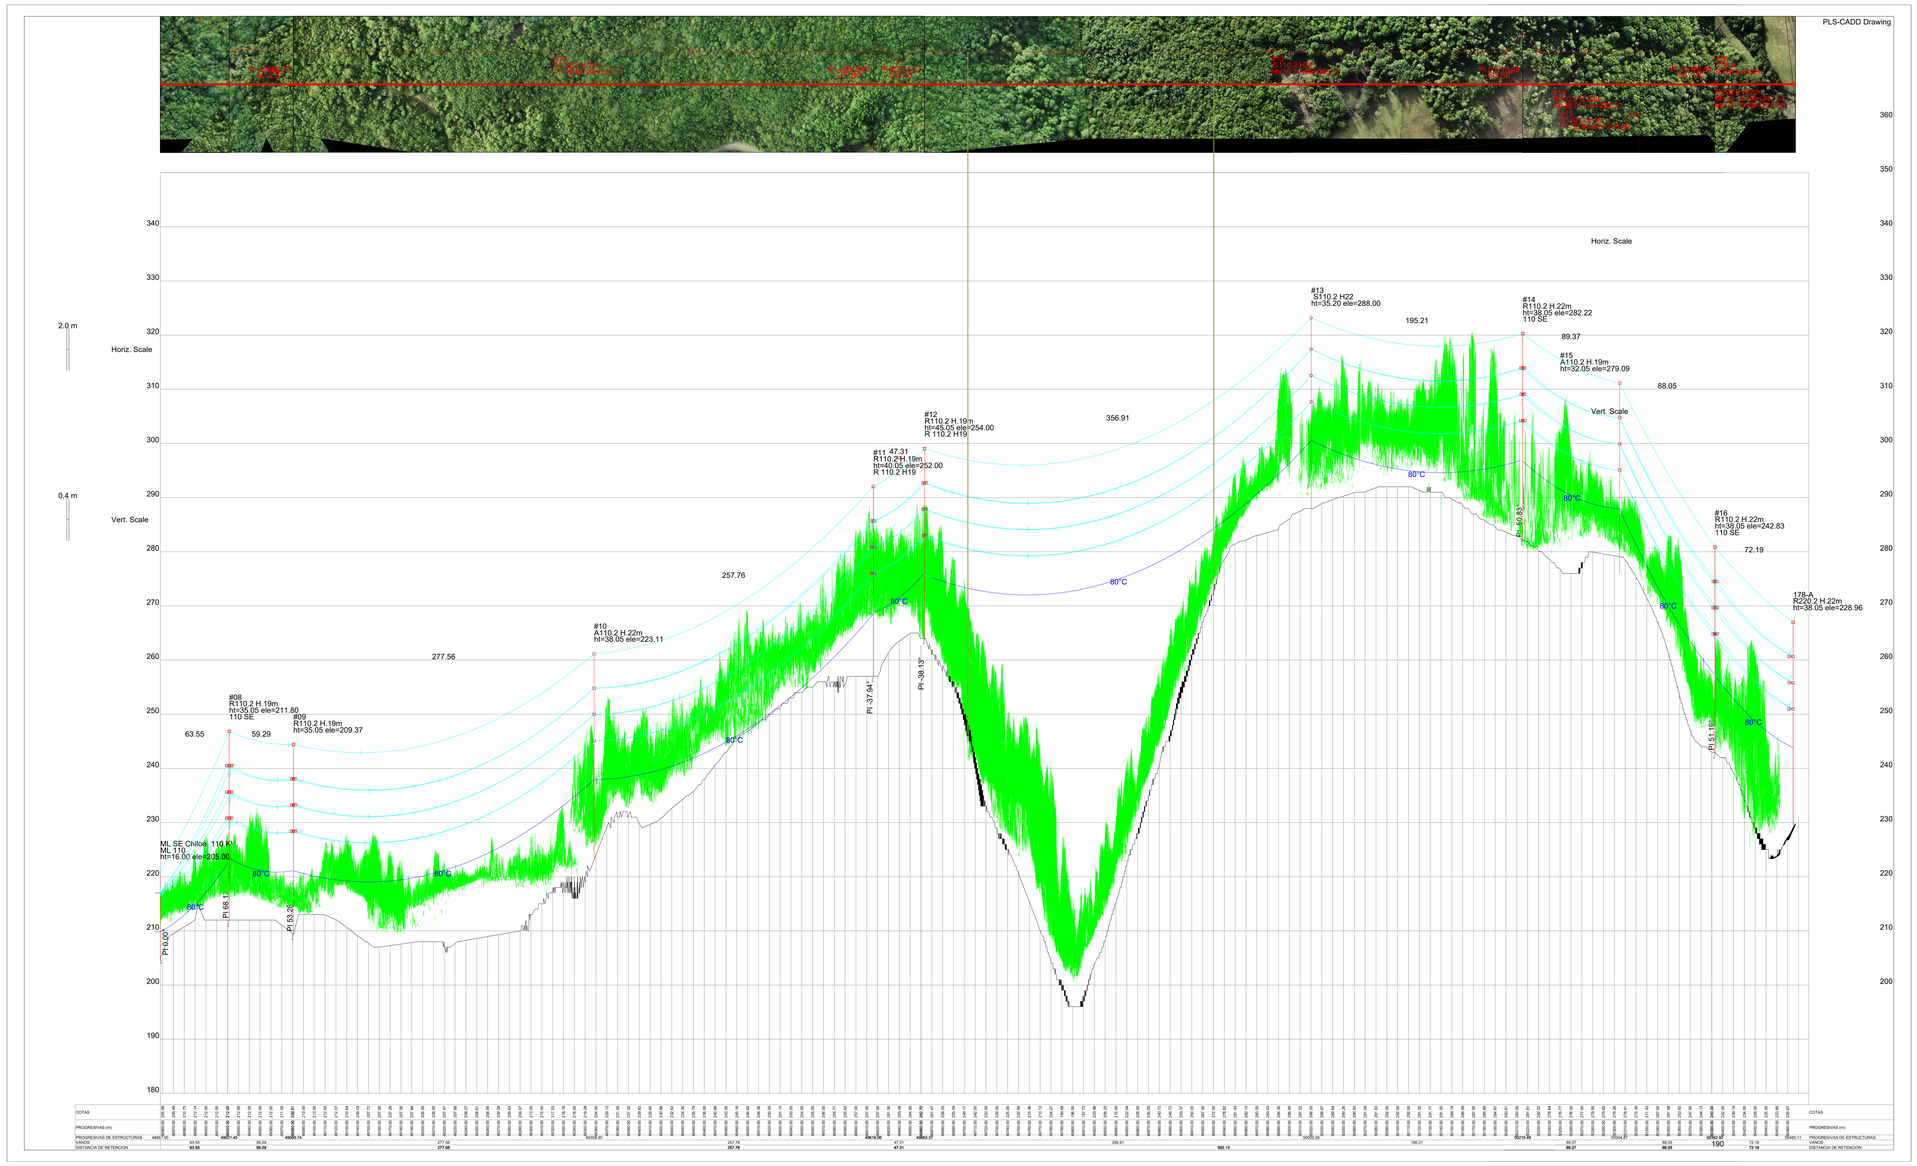
PLS-CADD Drawing
Horiz. Scale
Vert. Scale
2.0 m
0.4 m
#08
R110.2 H.19m
ht=35.05 ele=211.80
110 SE
#09
R110.2 H.19m
ht=35.05 ele=209.37
#10
A110.2 H.22m
ht=38.05 ele=223.11
#11
R110.2 H.19m
ht=40.05 ele=252.00
R 110.2 H19
#12
R110.2 H.19m
ht=45.05 ele=254.00
R 110.2 H19
#13
S110.2 H22
ht=35.20 ele=288.00
#14
R110.2 H.22m
ht=38.05 ele=282.22
110 SE
#15
A110.2 H.19m
ht=32.05 ele=279.09
#16
R110.2 H.22m
ht=38.05 ele=242.83
110 SE
178-A
R220.2 H.22m
ht=38.05 ele=228.96
ML SE Chiloé 110 K
ML 110
ht=16.00 ele=205.00
63.55
59.29
277.56
257.76
356.91
195.21
89.37
88.05
72.19
80°C
PI 0.00
PI 68.13
PI 53.28
PI -37.94°
PI -38.13°
PI 50.83
PI 51.19
COTAS
PROGRESIVAS (m)
PROGRESIVAS DE ESTRUCTURAS
VANOS
DISTANCIA DE RETENCION